
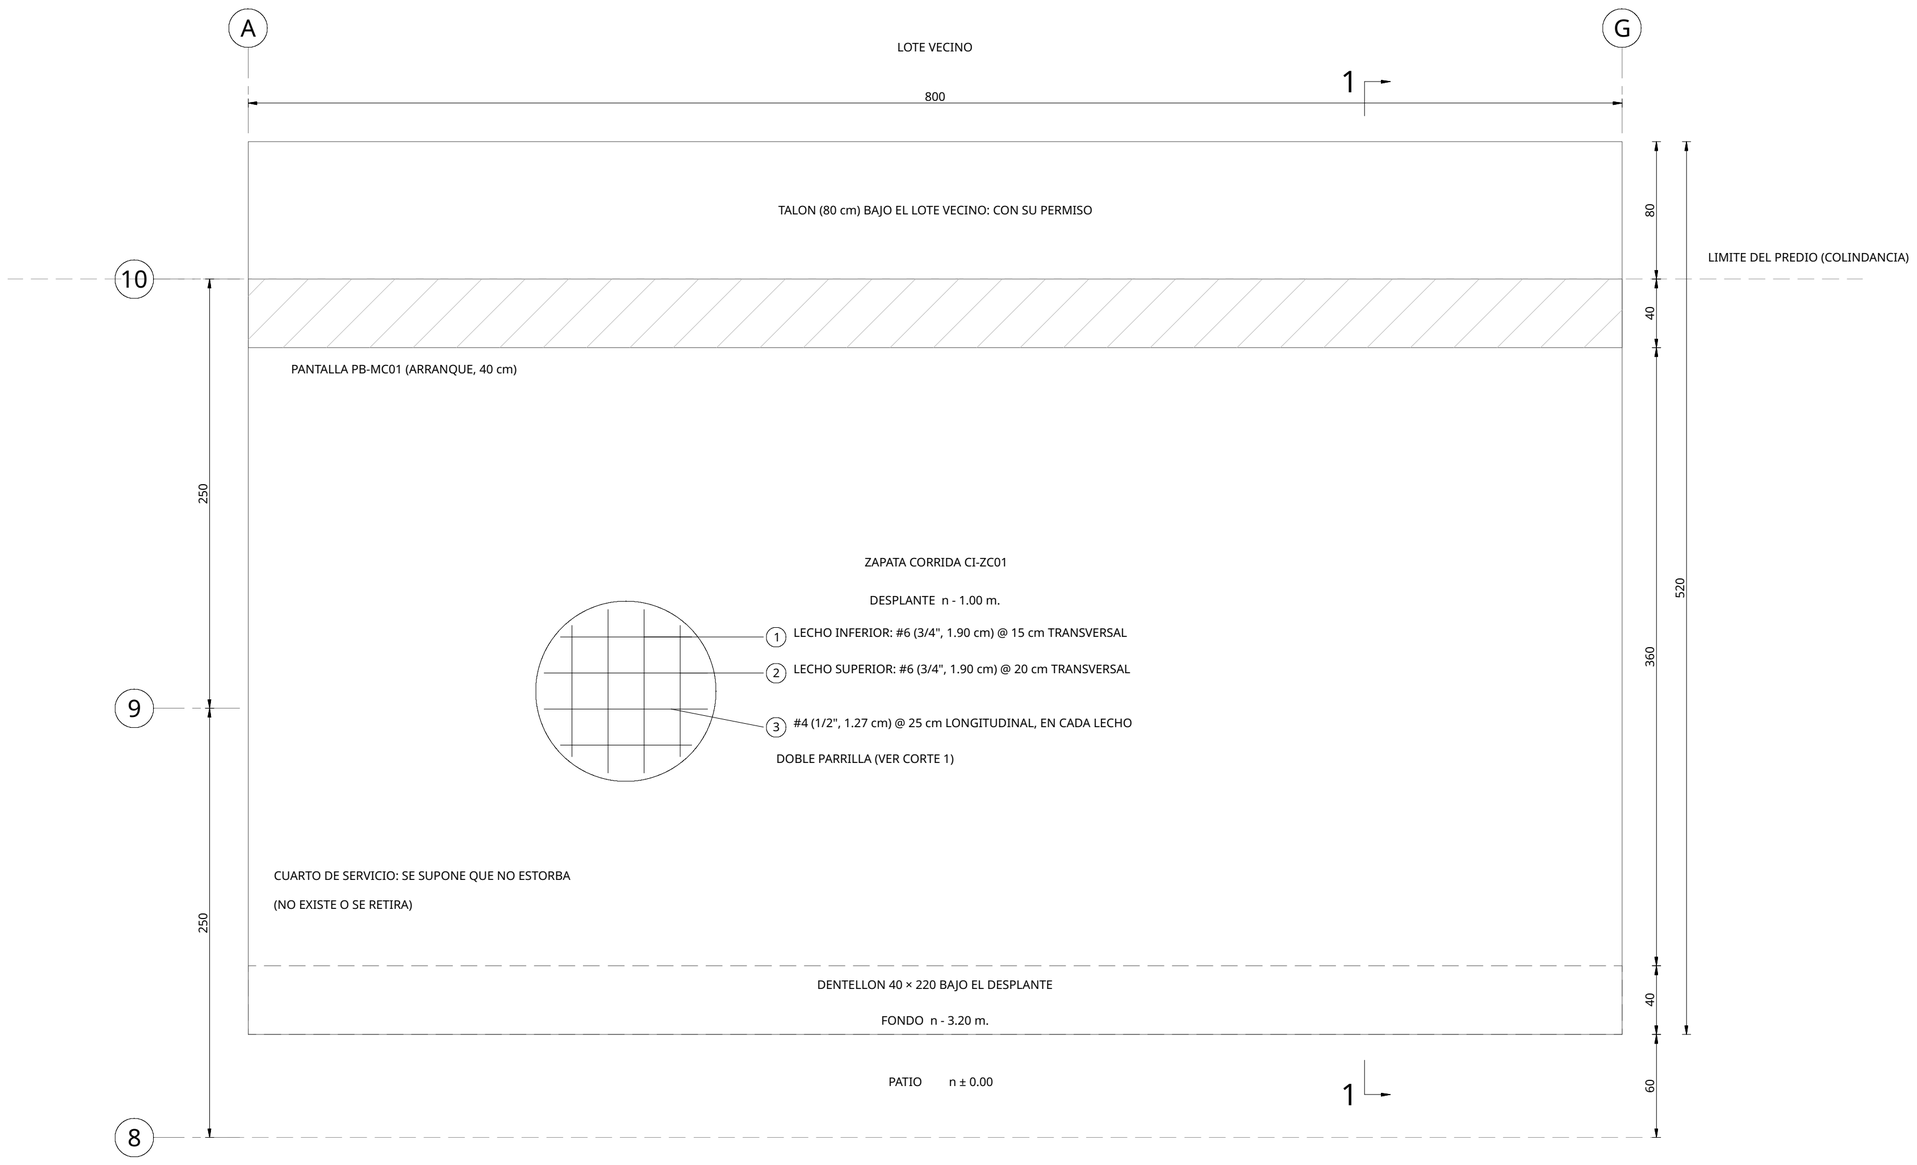


PLANTA DE CIMENTACION

CAPACIDAD DE CARGA ADMISIBLE DEL SUELO CONSIDERADA: Qadm = 7.5 t/m² (SUPUESTO, SIN ESTUDIO)
ZAPATA CORRIDA CON DENTELLON. DESPLANTE n - 1.00 m. EN TOBA. MEDIDAS: PROPUESTA DE ANTEPROYECTO

ESCALA 1 : 25

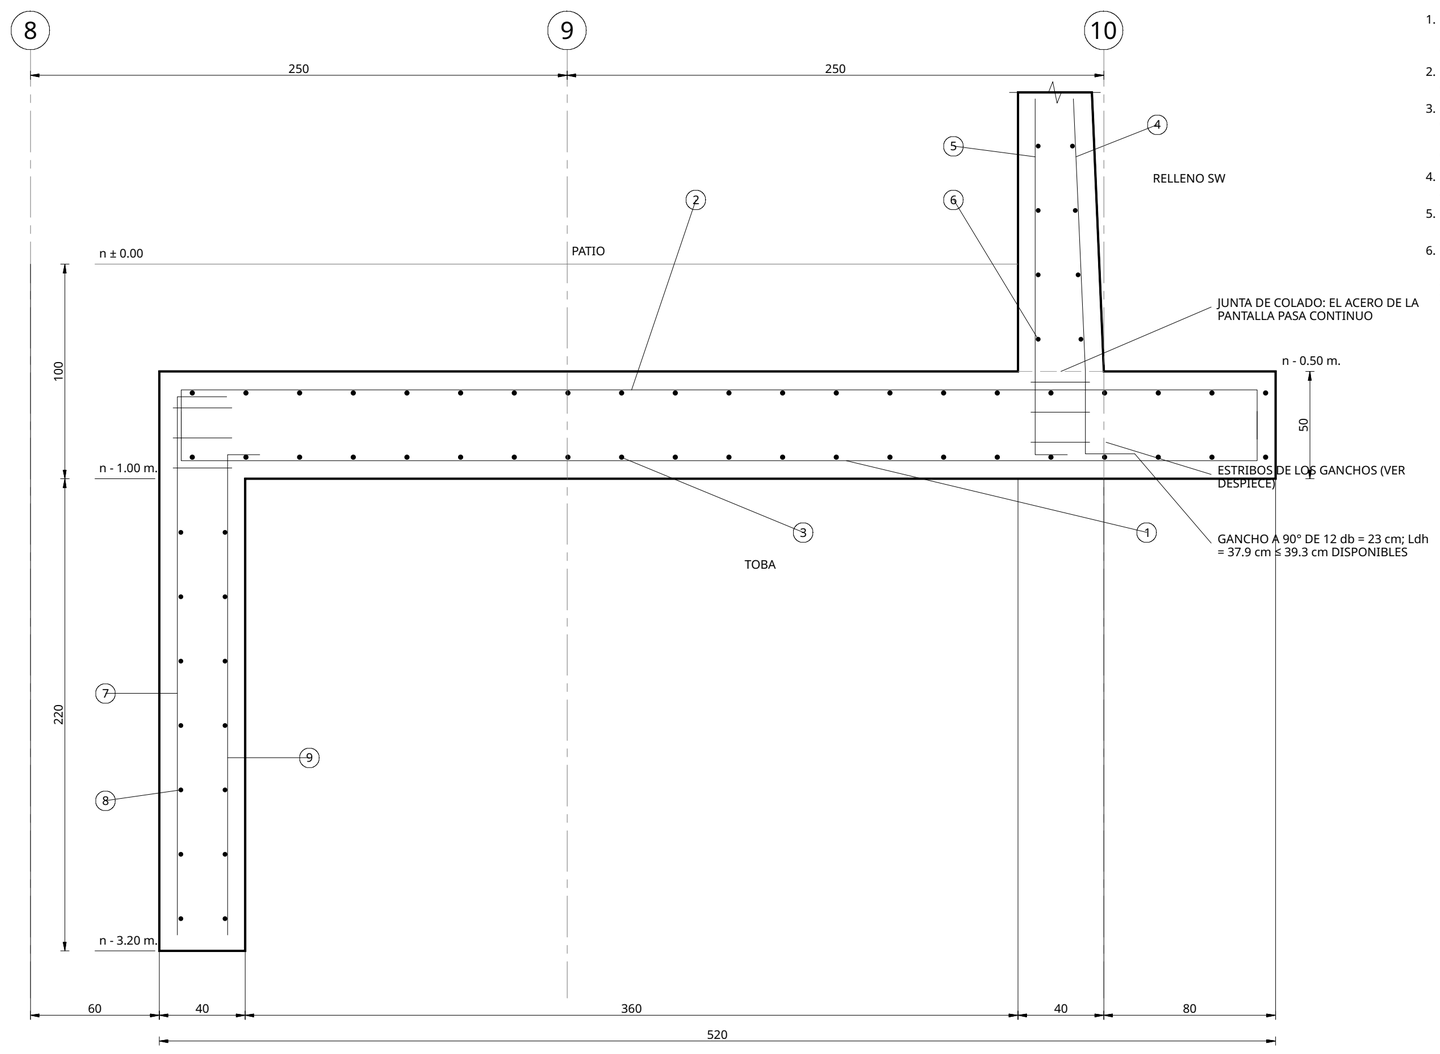

CONDICIONES DE LA CIMENTACION

1. NO SE EXCAVA NI SE CONSTRUYE ENTRE EL MURO Y LA CASA: EL DESLIZAMIENTO DEPENDE DEL PASIVO DEL DENTELLON (NTC-2023 CIMENTACIONES §6.2.1.3, p. 79).
2. EL TALON DE 80 cm QUEDA BAJO EL LOTE VECINO: SE CONSTRUYE CON EL PERMISO DEL VECINO.
3. EL DENTELLON SE EXCAVA HASTA n - 3.20 m. JUNTO A LA CIMENTACION DE LA CASA, CUYAS MEDIDAS NO SE CONOCEN: LA MECANICA DE SUELOS LO REVISA ANTES DE CONSTRUIR. SE CUELA CONTRA LA TOBA.
4. SE DEMUELE EL CIMIENTO DE MAMPOSTERIA DE LA BARDA CAIDA ANTES DE EXCAVAR (SUS MEDIDAS NO SE CONOCEN).
5. EL CUARTO DE SERVICIO SE SUPONE FUERA (NO EXISTE O SE RETIRA). SI ESTA, SE REVISA ANTES DE CONSTRUIR.
6. EL RELLENO QUEDA HORIZONTAL EN n + 3.00 m. AL MENOS 2.4 m DETRAS DEL TALON. SI EL PIE DEL TALUD QUEDA MAS CERCA, NO SE CORTA: SE DETIENE LA OBRA Y SE REVISA CON MECANICA DE SUELOS.

CORTE 1 - ZAPATA, DENTELLON Y ARRANQUE DE LA PANTALLA

ESCALA 1 : 20
TIPICO EN LOS 800 cm DEL MURO

DESPIECE DE LA CIMENTACION (CORTE 1) · MEDIDAS EN cm


MARCA	ELEMENTO	BARRA Y SEPARACION	FORMA	CROQUIS (SIN ESCALA)	LONGITUD (cm)	PIEZAS
1	ZAPATA, LECHO INFERIOR, TRANSVERSAL	#6 (3/4", 1.90 cm) @ 15 cm	RECTA 501; DOBLEZ A 90° DE 23 EN CADA EXTREMO, HACIA ARRIBA	23 — 501 — 23	547	53
2	ZAPATA, LECHO SUPERIOR, TRANSVERSAL	#6 (3/4", 1.90 cm) @ 20 cm	RECTA 501; DOBLEZ A 90° DE 23 EN CADA EXTREMO, HACIA ABAJO	501 / 23 — 23	547	40
3	ZAPATA, LONGITUDINAL, CADA LECHO	#4 (1/2", 1.27 cm) @ 25 cm	RECTA 785; DOBLEZ A 90° DE 15 EN CADA EXTREMO	15 — 785 — 15	815	42
4	PANTALLA, VERTICAL, CARA DEL RELLENO	#6 (3/4", 1.90 cm) @ 15 cm	343 POR LA CARA INCLINADA Y 39 RECTA HASTA LA PARRILLA; GANCHO A 90° DE 23 HACIA EL TALON	343 / 39 — 23	405	53
5	PANTALLA, VERTICAL, CARA DEL PATIO	#4 (1/2", 1.27 cm) @ 30 cm	RECTA 382; GANCHO A 90° DE 15 ABAJO, HACIA EL TALON	382 — 15	397	27
6	PANTALLA, HORIZONTAL, CADA CARA	#4 (1/2", 1.27 cm) @ 30 cm	RECTA 785; DOBLEZ A 90° DE 15 EN CADA EXTREMO	15 — 785 — 15	815	22
7	DENTELLON, VERTICAL, CARA DEL PASIVO	#6 (3/4", 1.90 cm) @ 15 cm	RECTA 251; GANCHO A 90° DE 23 ARRIBA, HACIA EL TALON	251 — 23	274	53
8	DENTELLON, HORIZONTAL, CADA CARA	#4 (1/2", 1.27 cm) @ 30 cm	RECTA 785; DOBLEZ A 90° DE 15 EN CADA EXTREMO	15 — 785 — 15	815	14
9	DENTELLON, VERTICAL, CARA DEL RELLENO	#4 (1/2", 1.27 cm) @ 30 cm	RECTA 223; GANCHO A 90° DE 15 ARRIBA, HACIA EL TALON	223 — 15	238	27

ESTRIBOS DE LOS GANCHOS DE LA PANTALLA: 3 ESTRIBOS CERRADOS #3 (3/8", 0.95 cm) HORIZONTALES @ 14 cm, EN 28 cm DE LA ALTURA DEL GANCHO, QUE ABRAZAN LAS BARRAS CON DOBLEZ
ESTRIBOS DE LOS GANCHOS DEL DENTELLON: 3 ESTRIBOS CERRADOS #3 (3/8", 0.95 cm) HORIZONTALES @ 14 cm, EN 28 cm DE LA ALTURA DEL GANCHO, QUE ABRAZAN LAS BARRAS CON DOBLEZ
NINGUNA BARRA LLEVA TRASLAPE: LA MAS LARGA MIDE 815 cm, MENOS QUE LA PIEZA COMERCIAL DE 12 m. GANCHOS Y DOBLECES A 90° DE 12 db. TODAS LAS BARRAS SON CONTINUAS.

NO APTO PARA CONSTRUCCION

PROPUESTA DE ANTEPROYECTO · PARAMETROS DE SUELO SUPUESTOS

DETALLES PARA ESTRIBOS

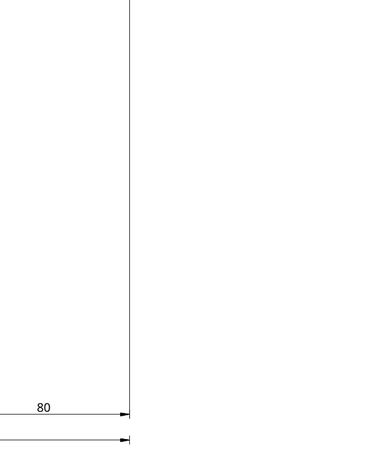

LONGITUDES DE ANCLAJE FINAL Y TRASLAPEANCLAJE FINAL

ANCLAJE FINAL GANCHO ESTANDAR A 90º

f'c = 250 kg/cm² — fy = 4,200 kg/cm²

VARILLA No.	Db	a	Ldh	b (cm) TRAMO RECTO	c (cm) EXTENSIÓN	R (cm) RADIO INTERIOR	D (cm) DIAMETRO EXTERIOR	DOBLEZ INCLUYENDO CURVA	La (cm)	Lt (cm)
3	0.95	19	14	11	4.2	10	17	34	40
4	1.27	26	19	15	5.6	14	22	45	56
5	1.59	32	23	19	7.0	17	28	56	60
6	1.90	38	28	23	8.4	21	33	67	75
8	2.54	51	37	30	11.2	28	44	90	107

La (cm):
LONGITUD TOTAL DE ANCLAJE FINAL A PARTIR DE LA SECCION CRITICA

NOTA:
USAR "La" COMO LONGITUD DE ANCLAJE FINAL MINIMA, EN CASO QUE LA LONGITUD "a" PUEDA DARSE; EN CASO CONTRARIO SE DEBERÁ DE USAR "Lt" COMO LONGITUD DE ANCLAJE FINAL MINIMA.

NOTAS Y ESPECIFICACIONES

1 PARAMETROS DE SUELO SUPUESTOS: NO APTO PARA CONSTRUCCION. NO SE CONSTRUYÉ HASTA REVISARLO CON UNA MECANICA DE SUELOS
2 CONCRETO CLASE 1, f'c = 250 kg/cm², EXPOSICION A2, CURADO CON AGUA 7 DIAS
3 ACERO DE REFUERZO A.S.T.M. A-615 GRADO 42 (fy = 4,200 kg/cm²) PARA TODOS LOS DIAMETROS
4 RECUBRIMIENTO LIBRE: 75 mm EN ZAPATA Y PANTALLA (NTC-2023 CONCRETO TABLA 9.2.2.2)
5 CAPACIDAD DE CARGA ADMISIBLE DEL SUELO: 7.5 t/m² (SUPUESTO, SIN ESTUDIO DE MECANICA DE SUELOS)
6 DESPLANTE: 100 cm BAJO EL PATIO, EN TOBA. PASIVO DEL DENTELLON CON φ = 17° Y γ = 1.58 t/m³ (SUPUESTOS)
7 NO EXCAVAR AL PIE DEL MURO NI DEL DENTELLON: EL DESLIZAMIENTO DEPENDE DE SU PASIVO
8 EL RELLENO SERA ARENA BIEN GRADUADA (SW), COMPACTADA POR CAPAS; EL FILTRO, EL TUBO Y LOS LLORADEROS SON CONDICION DEL DISEÑO
9 BARDA DE NOVABLOCK MULTIPERFORADO 10 DE NOVACERAMIC (32.5 × 20 × 10 cm); APLANADO ± 1.5 cm POR CARA. LA FICHA TECNICA DEL FABRICANTE ACREDITA f_an ≥ 0.50
10 LA LOCALIZACION DEL REMATE DEL ESTRIBO DE CUALQUIER ELEMENTO DEBERA ALTERNARSE DE UNO A OTRO LADO DEL MISMO
11 NO TOMAR MEDIDAS A ESCALA. LAS COTAS RIGEN AL DIBUJO. COTAS Y ARMADOS EN cm, TAMBIEN EL ACERO; NIVELES EN m
12 PROPUESTA DE ANTEPROYECTO PARA TRAMITE DE SEGURO. LIMITACIONES Y SUPUESTOS DECLARADOS EN LA MEMORIA DE CALCULO
13 EL ORIGINAL DE ESTE PLANO ES PROPIEDAD Y RESPONSABILIDAD EXCLUSIVA DEL CALCULISTA QUE FIRMA ESTA COPIA. CUALQUIER MODIFICACION DE SECCIONES, ARMADOS Y/O MODIFICACIONES ARQUITECTONICAS, DEBERAN SER PREVIAMENTE CONSULTADAS AL CALCULISTA, EL CUAL DARÁ SU APROBACIÓN O RECHAZO POR ESCRITO. DOCUMENTO QUE SE ANEXARA A ESTE PLANO, EN CASO DE NO SER ASÍ, EL CALCULISTA SE VERÁ LIBERADO DE TODA RESPONSABILIDAD INHERENTE A ESTE PROYECTO
14 EL CONSTRUCTOR DE LA OBRA, SERÁ EL RESPONSABLE DE LA CORRECTA INTERPRETACIÓN DEL PLANO, ASÍ COMO DE LA CALIDAD Y CARACTERÍSTICAS DE LOS MATERIALES EMPLEADOS, TANTO POR SU PERSONAL, COMO POR LOS SUBCONTRATISTAS Y DESTAJISTAS QUE INTERVENGAN EN LA EJECUCION DE LA OBRA
15 EL PROPIETARIO Y EL OCUPANTE DE LA CONSTRUCCIÓN, SERÁN LOS RESPONSABLES DEL USO DE LA MISMA, Y DE QUE LAS CARGAS VIVAS ESTIPULADAS EN LOS PLANOS NO SEAN EXCEDIDAS

CLAVE DE ELEMENTOS

- PANTALLA, ZAPATA Y DENTELLON DE CONCRETO
- BARDA DE NOVABLOCK MULTIPERFORADO 10
- CASTILLO Y DALA DE LA BARDA
- POR DEMOLER (BARDA CAIDA)

PROYECTO ESTRUCTURAL

M.I. FRANCISCO JAVIER CISNEROS RUIZ
CED. PROF. 15747504
MAESTRIA EN ESTRUCTURAS, UNAM

PROYECTO: MURO DE CONTENCION

PROPIETARIO

ESTADO: ANTEPROYECTO

UBICACION: COATEPEC, VER.


PLANO DE: CIMENTACION

FECHA: OCTUBRE 2026

ACOTACIONES: CENTIMETROS

ESCALA: INDICADA


CLAVE DE PLANO: E-1

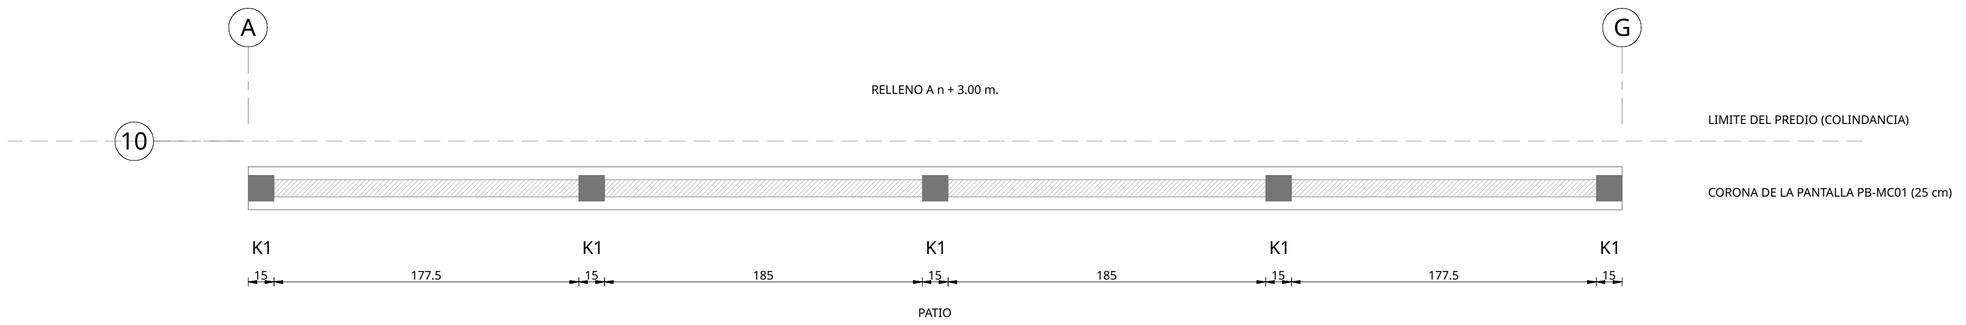

PLANTA DE LA BARDA

A NIVEL DE LA CORONA DEL MURO, n + 3.00 m.: LA BARDA PB-M01 Y SUS 5 CASTILLOS K1 SOBRE LA PANTALLA


ESCALA 1 : 25

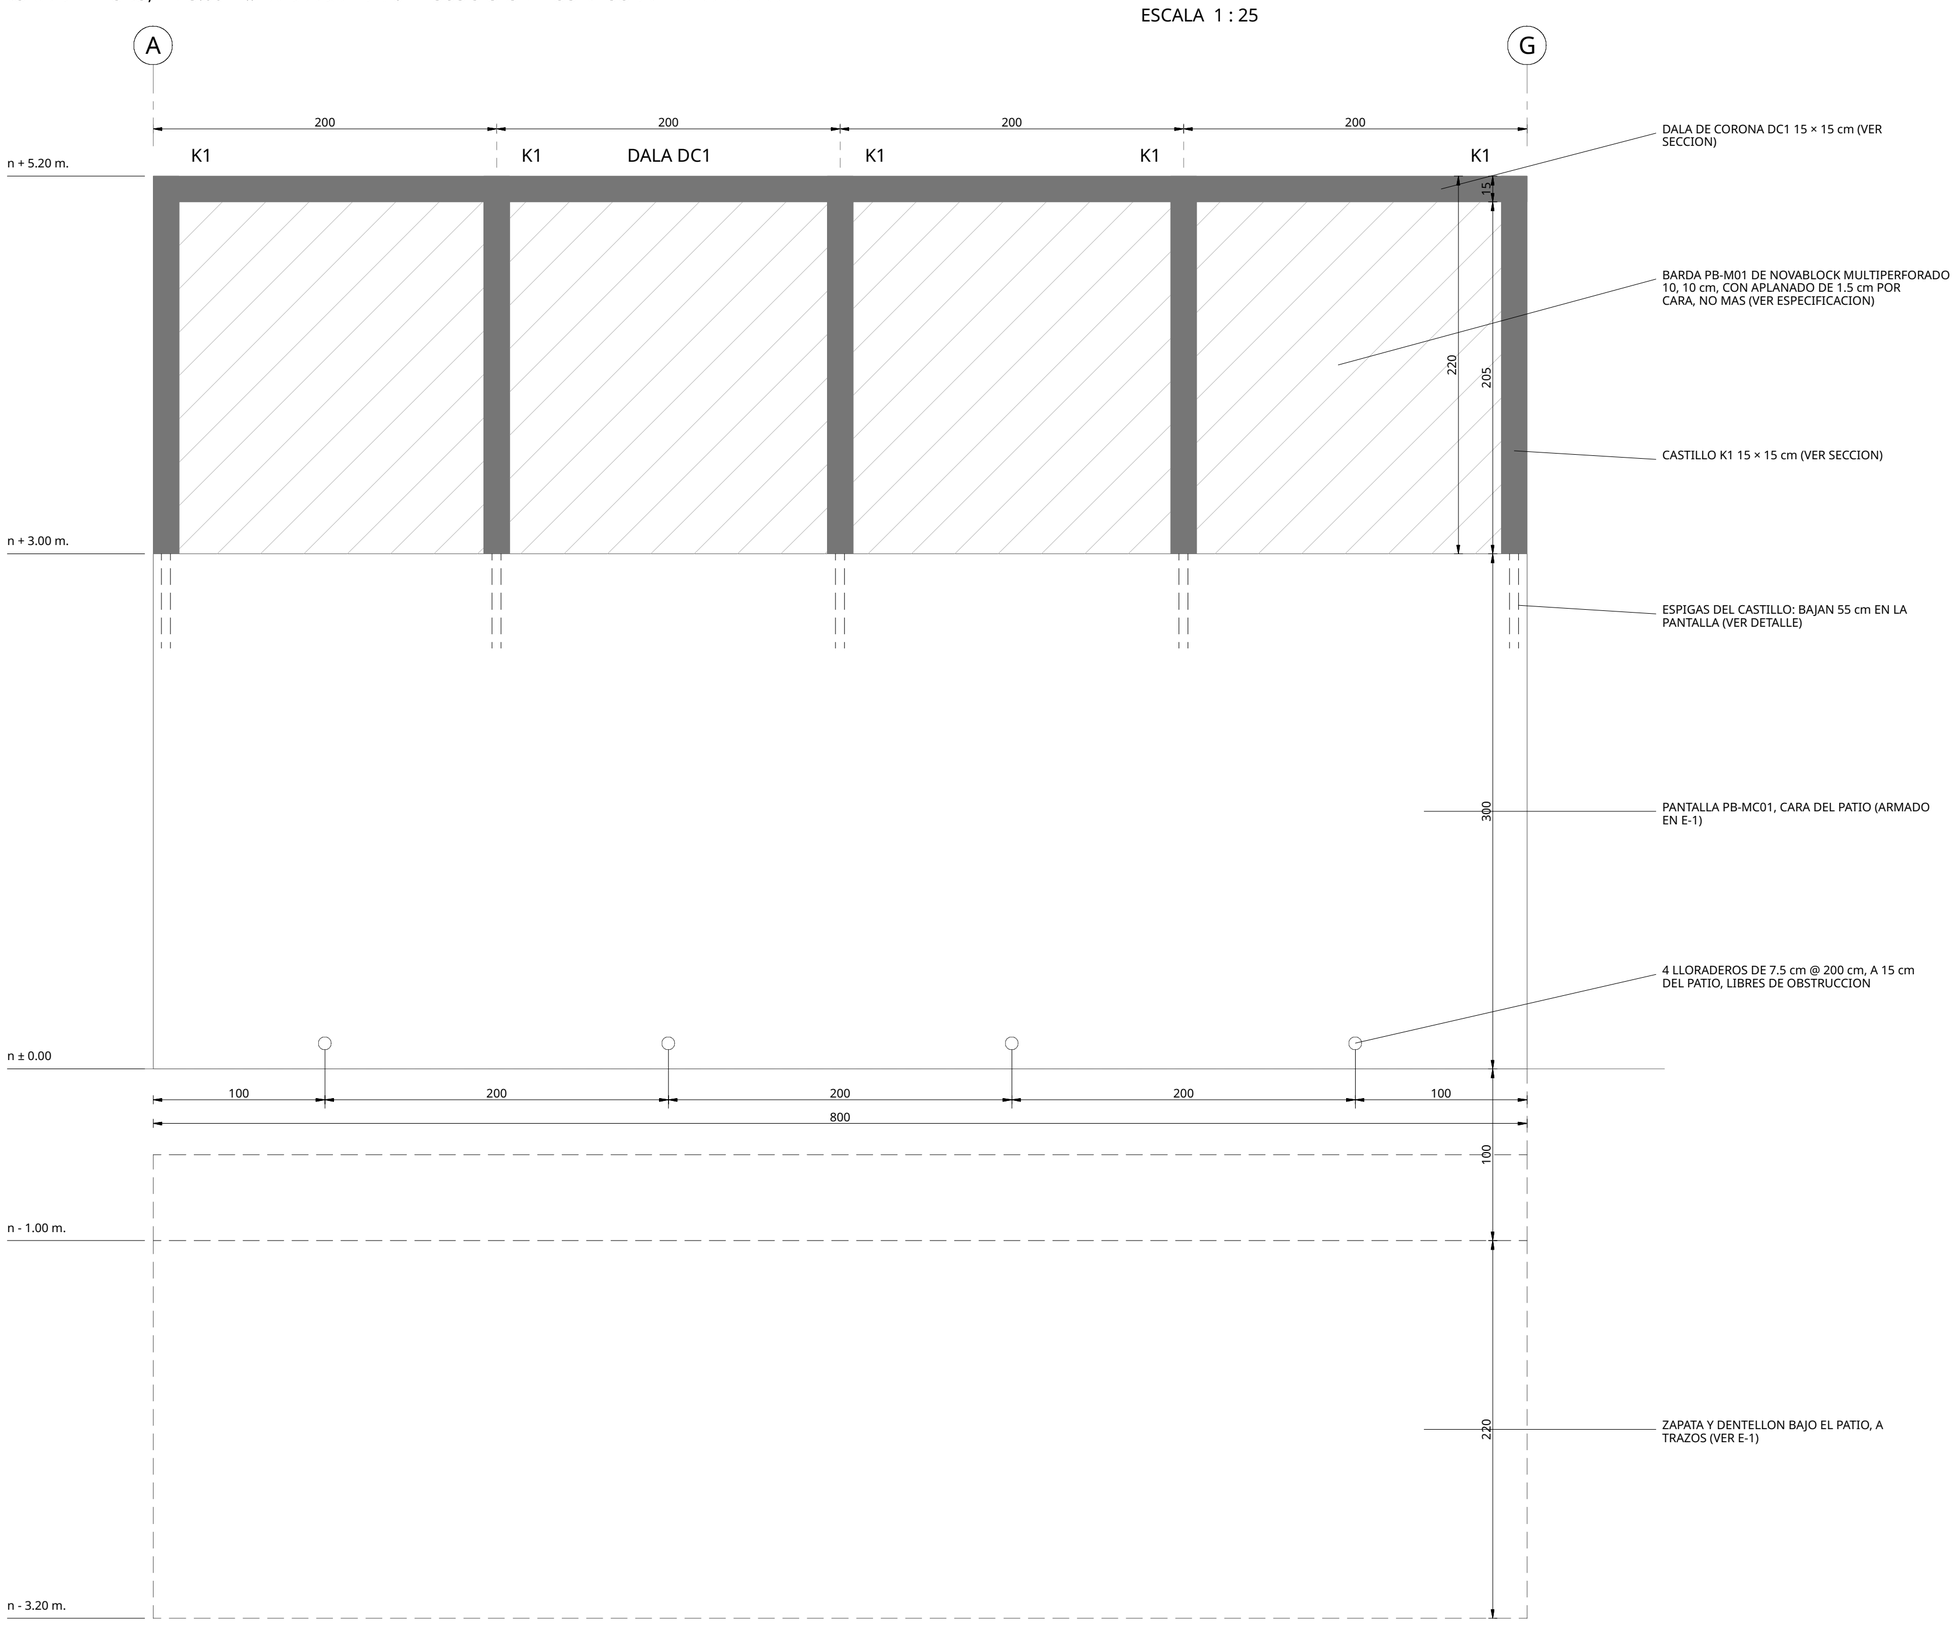

ALZADO DEL MURO Y LA BARDA

VISTO DESDE EL PATIO

ESCALA 1 : 25

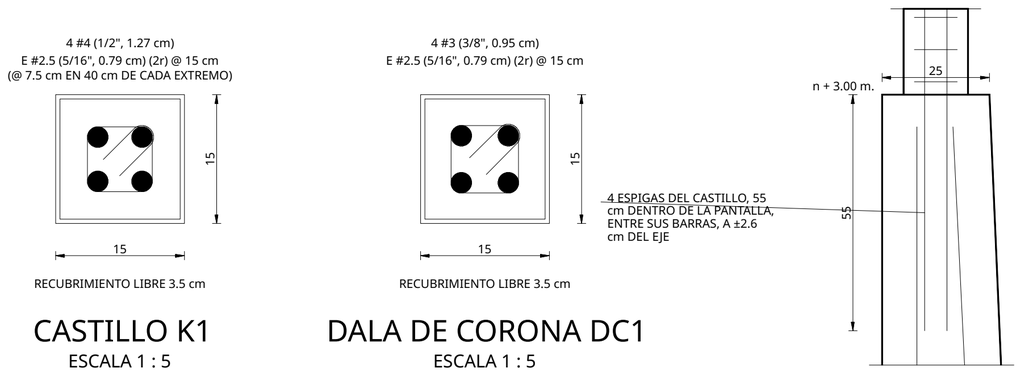

CASTILLO K1

ESCALA 1 : 5

DALA DE CORONA DC1

ESCALA 1 : 5

ARRANQUE DEL CASTILLO K1

ESCALA 1 : 10

ESPECIFICACION DE LA BARDA PB-M01

1. NOVABLOCK MULTIPERFORADO 10 DE NOVACERAMIC: PIEZA HUECA MULTIPERFORADA DE ARCILLA EXTRUIDA, 32.5 × 20 × 10 cm, DE 10 cm, CON APLANADO DE 1.5 cm DE MORTERO DE CEMENTO Y ARENA EN CADA CARA; PIEZA HUECA MULTIPERFORADA CON f_an ≥ 0.50, PARED EXTERIOR ≥ 15 mm, INTERIOR ≥ 7 mm Y PESO VOLUMÉTRICO NETO ≥ 1 700 kg/m³, ACREDITADOS CON FICHA TÉCNICA SEGÚN LA NMX-C-404-ONNCCE-2012; fp ≥ 120 kg/cm²; MORTERO TIPO I O II Y JUNTA DE 10 A 12 mm; ESTRUCTURA TIPO II
2. APLANADO DE 1.5 cm POR CARA, NO MAS: EL MURO SE REVISO CON ESE PESO.
3. 5 CASTILLOS DE 15 × 15 cm @ 200 cm, CON 4 #4 (1/2", 1.27 cm) Y ESTRIBOS #2.5 (5/16", 0.79 cm) @ 15 cm; LAS 4 BARRAS DEL CASTILLO BAJAN 55 cm DENTRO DE LA PANTALLA, INTERCALADAS CON SUS BARRAS.
4. DALA DE CORONA DE 15 × 15 cm CON 4 #3 (3/8", 0.95 cm) Y ESTRIBOS #2.5 (5/16", 0.79 cm) @ 15 cm.


DETALLES PARA ESTRIBOS



LONGITUDES DE ANCLAJE FINAL Y TRASLAPEANCLAJE FINAL ANCLAJE FINAL GANCHO ESTANDAR A 90º

f'c = 250 kg/cm² fy = 4,200 kg/cm²

VARILLA No.	Db	a	Ldh	b (cm) TRAMO RECTO	c (cm) EXTENSIÓN	R (cm) RADIO INTERIOR	D (cm) DIAMETRO EXTERIOR	DOBLEZ INCLUYENDO CURVA	La (cm)	Lt (cm)
3	0.95	19	14	11	4.2	10	17	34	40	
4	1.27	26	19	15	5.6	14	22	45	56	
5	1.59	32	23	19	7.0	17	28	56	60	
6	1.90	38	28	23	8.4	21	33	67	75	
8	2.54	51	37	30	11.2	28	44	90	107	

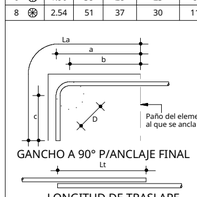

La (cm):
LONGITUD TOTAL DE ANCLAJE FINAL A PARTIR DE LA SECCION CRITICA

NOTA:
USAR "La" COMO LONGITUD DE ANCLAJE FINAL MINIMA, EN CASO QUE LA LONGITUD "a" PUEDA DARSE; EN CASO CONTRARIO SE DEBERÁ DE USAR "Lt" COMO LONGITUD DE ANCLAJE FINAL MINIMA.

NO APTO PARA CONSTRUCCION

PROPUESTA DE ANTEPROYECTO · PARAMETROS DE SUELO SUPUESTOS

NOTAS Y ESPECIFICACIONES

1 PARAMETROS DE SUELO SUPUESTOS: NO APTO PARA CONSTRUCCION. NO SE CONSTRUYE HASTA REVISARLO CON UNA MECANICA DE SUELOS
2 CONCRETO CLASE 1, f'c = 250 kg/cm², EXPOSICION A2, CURADO CON AGUA 7 DIAS
3 ACERO DE REFUERZO A.S.T.M. A-615 GRADO 42 (fy = 4,200 kg/cm²) PARA TODOS LOS DIAMETROS
4 RECUBRIMIENTO LIBRE: 75 mm EN ZAPATA Y PANTALLA (NTC-2023 CONCRETO TABLA 9.2.2.2)
5 CAPACIDAD DE CARGA ADMISIBLE DEL SUELO: 7.5 t/m² (SUPUESTO, SIN ESTUDIO DE MECANICA DE SUELOS)
6 DESPLANTE: 100 cm BAJO EL PATIO, EN TOBA. PASIVO DEL DENTELLON CON φ = 17° Y γ = 1.58 t/m³ (SUPUESTOS)
7 NO EXCAVAR AL PIE DEL MURO NI DEL DENTELLON: EL DESLIZAMIENTO DEPENDE DE SU PASIVO
8 EL RELLENO SERA ARENA BIEN GRADUADA (SW), COMPACTADA POR CAPAS; EL FILTRO, EL TUBO Y LOS LLORADEROS SON CONDICION DEL DISEÑO
9 BARDA DE NOVABLOCK MULTIPERFORADO 10 DE NOVACERAMIC (32.5 × 20 × 10 cm); APLANADO ≤ 1.5 cm POR CARA. LA FICHA TECNICA DEL FABRICANTE ACREDITA f_an ≥ 0.50
10 LA LOCALIZACION DEL REMATE DEL ESTRIBO DE CUALQUIER ELEMENTO DEBERA ALTERNARSE DE UNO A OTRO LADO DEL MISMO
11 NO TOMAR MEDIDAS A ESCALA. LAS COTAS RIGEN AL DIBUJO. COTAS Y ARMADOS EN cm, TAMBIEN EL ACERO; NIVELES EN m
12 PROPUESTA DE ANTEPROYECTO PARA TRAMITE DE SEGURO. LIMITACIONES Y SUPUESTOS DECLARADOS EN LA MEMORIA DE CALCULO
13 EL ORIGINAL DE ESTE PLANO ES PROPIEDAD Y RESPONSABILIDAD EXCLUSIVA DEL CALCULISTA QUE FIRMA ESTA COPIA, CUALQUIER MODIFICACION DE SECCIONES, ARMADOS Y/O MODIFICACIONES ARQUITECTONICAS, DEBERAN SER PREVIAMENTE CONSULTADAS AL CALCULISTA, EL CUAL DARÁ SU APROBACIÓN O RECHAZO POR ESCRITO, DOCUMENTO QUE SE ANEXARA A ESTE PLANO, EN CASO DE NO SER ASÍ, EL CALCULISTA SE VERÁ LIBERADO DE TODA RESPONSABILIDAD INHERENTE A ESTE PROYECTO
14 EL CONSTRUCTOR DE LA OBRA, SERÁ EL RESPONSABLE DE LA CORRECTA INTERPRETACIÓN DEL PLANO, ASÍ COMO DE LA CALIDAD Y CARACTERÍSTICAS DE LOS MATERIALES EMPLEADOS, TANTO POR SU PERSONAL, COMO POR LOS SUBCONTRATISTAS Y DESTAJISTAS QUE INTERVENGAN EN LA EJECUCION DE LA OBRA
15 EL PROPIETARIO Y EL OCUPANTE DE LA CONSTRUCCIÓN, SERÁN LOS RESPONSABLES DEL USO DE LA MISMA, Y DE QUE LAS CARGAS VIVAS ESTIPULADAS EN LOS PLANOS NO SEAN EXCEDIDAS

CLAVE DE ELEMENTOS

- PANTALLA, ZAPATA Y DENTELLON DE CONCRETO
- BARDA DE NOVABLOCK MULTIPERFORADO 10
- CASTILLO Y DALA DE LA BARDA
- POR DEMOLER (BARDA CAIDA)

PROYECTO ESTRUCTURAL

M.I. FRANCISCO JAVIER CISNEROS RUIZ
CED. PROF. 15747594
MAESTRIA EN ESTRUCTURAS, UNAM

PROYECTO: MURO DE CONTENCION

PROPIETARIO

ESTADO: ANTEPROYECTO

UBICACION: COATEPEC, VER.


PLANO DE: MURO Y BARDA POR NIVELES

FECHA: OCTUBRE 2026

ACOTACIONES: CENTIMETROS

ESCALA: INDICADA


CLAVE DE PLANO: E-2

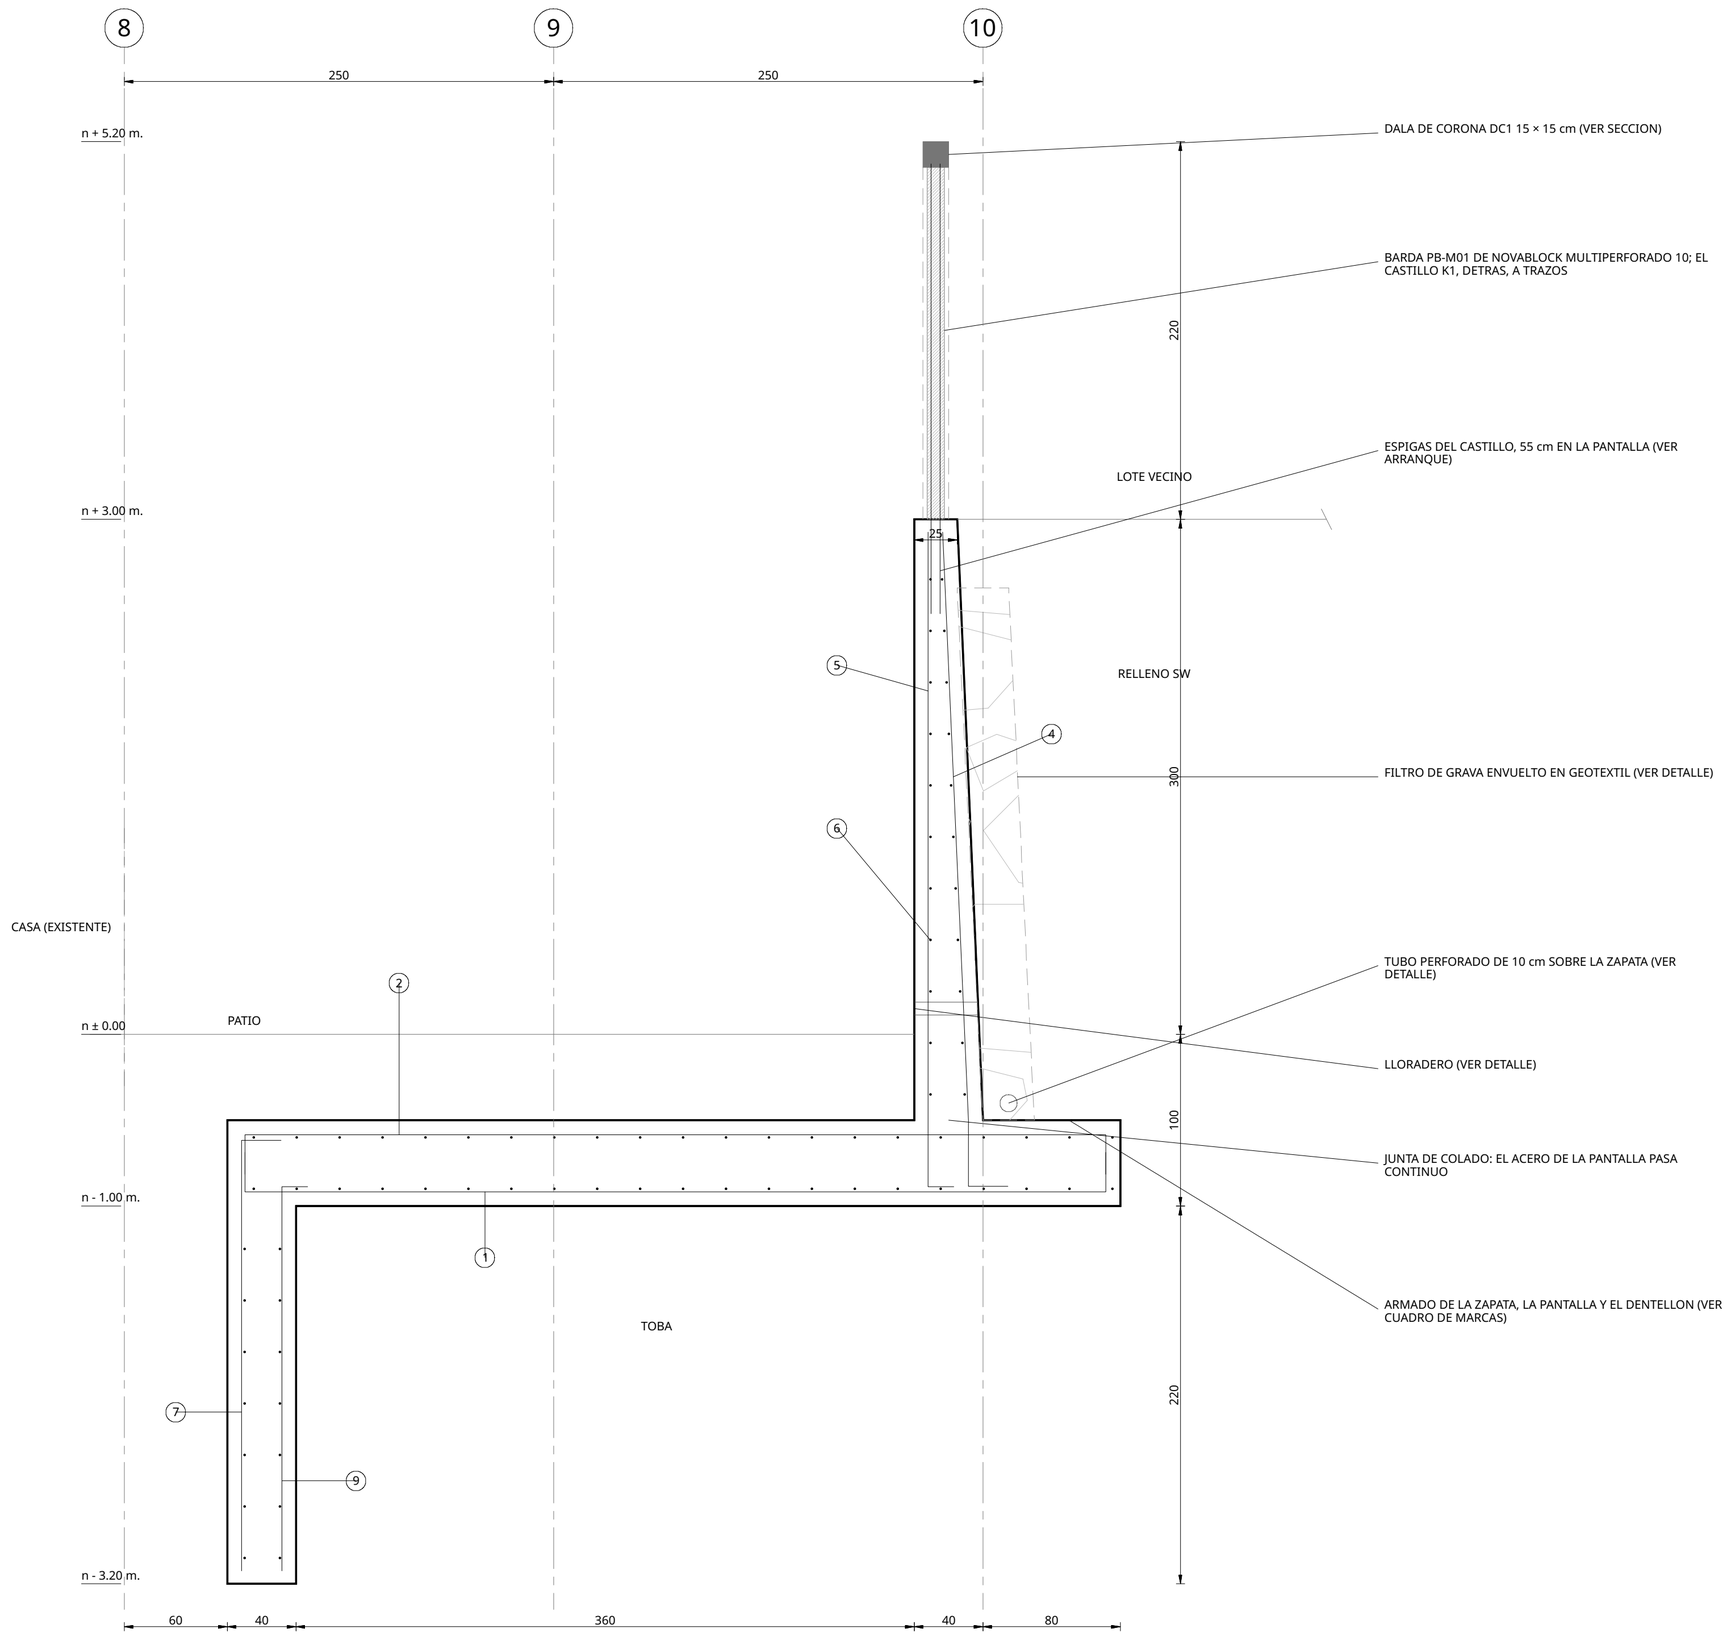

CORTE 2 - TRANSVERSAL DEL MURO

ESCALA 1 : 25

TIPICO EN LOS 800 cm

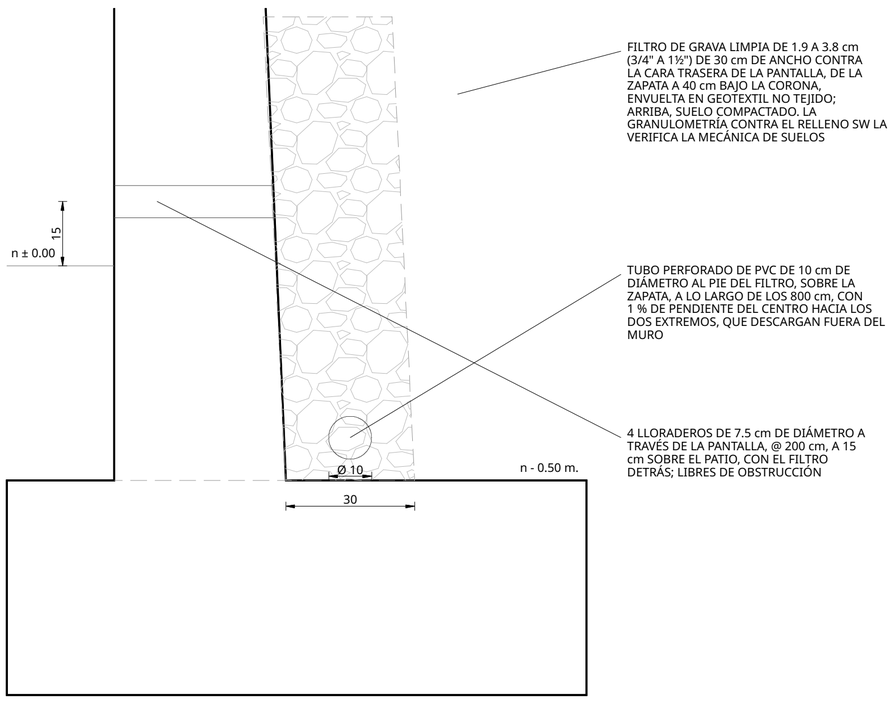


DETALLE DEL DRENAJE

ESCALA 1 : 10


JUNTAS

1. JUNTA DE COLADO HORIZONTAL ENTRE LA ZAPATA Y LA PANTALLA, A LA CARA SUPERIOR DE LA ZAPATA, CON EL ACERO DE LA PANTALLA CONTINUO; SUPERFICIE RUGOSA, LIMPIA Y HUMEDECIDA. SI EL COLADO SE PARTE A LO LARGO, LA JUNTA VERTICAL VA A A 400 cm, CON EL ACERO HORIZONTAL CONTINUO
2. SIN JUNTAS DE DILATACIÓN NI DE CONTRACCIÓN EN LOS 800 cm: EL ACERO DE TEMPERATURA CONTROLA EL AGRIETAMIENTO Y LA NORMA NO FIJA UNA SEPARACIÓN; SE DECLARA SUPUESTO

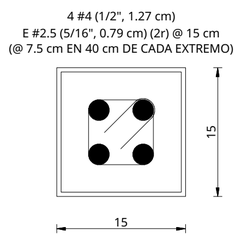


CASTILLO K1

ESCALA 1 : 5

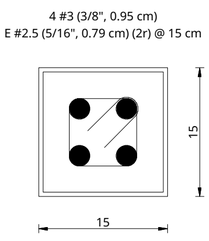

DALA DE CORONA DC1

ESCALA 1 : 5

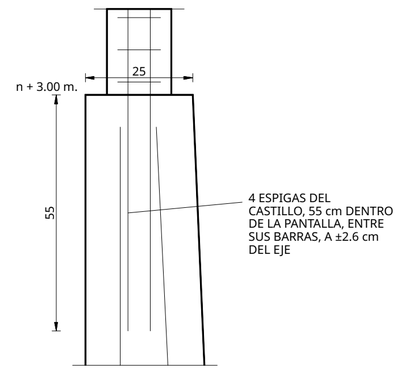

ARRANQUE DEL CASTILLO K1

ESCALA 1 : 10


MARCAS DEL ARMADO (CORTE 2)

MARCA	ELEMENTO	BARRA Y SEPARACION
1	ZAPATA, LECHO INFERIOR, TRANSVERSAL	#6 (3/4", 1.90 cm) @ 15 cm
2	ZAPATA, LECHO SUPERIOR, TRANSVERSAL	#6 (3/4", 1.90 cm) @ 20 cm
3	ZAPATA, LONGITUDINAL, CADA LECHO	#4 (1/2", 1.27 cm) @ 25 cm
4	PANTALLA, VERTICAL, CARA DEL RELLENO	#6 (3/4", 1.90 cm) @ 15 cm
5	PANTALLA, VERTICAL, CARA DEL PATIO	#4 (1/2", 1.27 cm) @ 30 cm
6	PANTALLA, HORIZONTAL, CADA CARA	#4 (1/2", 1.27 cm) @ 30 cm
7	DENTELLON, VERTICAL, CARA DEL PASIVO	#6 (3/4", 1.90 cm) @ 15 cm
8	DENTELLON, HORIZONTAL, CADA CARA	#4 (1/2", 1.27 cm) @ 30 cm
9	DENTELLON, VERTICAL, CARA DEL RELLENO	#4 (1/2", 1.27 cm) @ 30 cm

NO APTO PARA CONSTRUCCION

PROPUESTA DE ANTEPROYECTO · PARAMETROS DE SUELO SUPUESTOS


DETALLES PARA ESTRIBOS

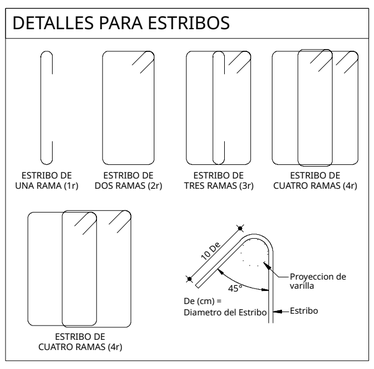

LONGITUDES DE ANCLAJE FINAL Y TRASLAPEANCLAJE FINAL ANCLAJE FINAL GANCHO ESTANDAR A 90º

f'c = 250 kg/cm² fy = 4,200 kg/cm²

VARILLA No.	Db	a	Ldh	b (cm) TRAMO RECTO	c (cm) EXTENSION	R (cm) RADIO INTERIOR	D (cm) DIAMETRO EXTERIOR	DOBLEZ INCLUYENDO CURVA	La (cm)	Lt (cm)
3	0.95	19		14	11	4.2	10	17	34	40
4	1.27	26		19	15	5.6	14	22	45	56
5	1.59	32		23	19	7.0	17	28	56	60
6	1.90	38		28	23	8.4	21	33	67	75
8	2.54	51		37	30	11.2	28	44	90	107

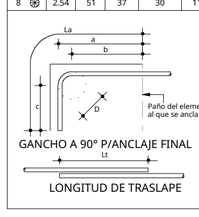

La (cm):
LONGITUD TOTAL DE ANCLAJE FINAL A PARTIR DE LA SECCION CRITICA

NOTA:
USAR "La" COMO LONGITUD DE ANCLAJE FINAL MINIMA, EN CASO QUE LA LONGITUD "a" PUEDA DARSE; EN CASO CONTRARIO SE DEBERÁ DE USAR "Lt" COMO LONGITUD DE ANCLAJE FINAL MINIMA.

NOTAS Y ESPECIFICACIONES

1 PARAMETROS DE SUELO SUPUESTOS: NO APTO PARA CONSTRUCCION. NO SE CONSTRUYE HASTA REVISARLO CON UNA MECANICA DE SUELOS
2 CONCRETO CLASE 1, f'c = 250 kg/cm², EXPOSICION A2, CURADO CON AGUA 7 DIAS
3 ACERO DE REFUERZO A.S.T.M. A-615 GRADO 42 (fy = 4,200 kg/cm²) PARA TODOS LOS DIAMETROS
4 RECUBRIMIENTO LIBRE: 75 mm EN ZAPATA Y PANTALLA (NTC-2023 CONCRETO TABLA 9.2.2.2)
5 CAPACIDAD DE CARGA ADMISIBLE DEL SUELO: 7.5 t/m² (SUPUESTO, SIN ESTUDIO DE MECANICA DE SUELOS)
6 DESPLANTE: 100 cm BAJO EL PATIO, EN TOBA. PASIVO DEL DENTELLON CON φ = 17° Y γ = 1.58 t/m³ (SUPUESTOS)
7 NO EXCAVAR AL PIE DEL MURO NI DEL DENTELLON: EL DESLIZAMIENTO DEPENDE DE SU PASIVO
8 EL RELLENO SERA ARENA BIEN GRADUADA (SW), COMPACTADA POR CAPAS; EL FILTRO, EL TUBO Y LOS LLORADEROS SON CONDICION DEL DISEÑO
9 BARDA DE NOVABLOCK MULTIPERFORADO 10 DE NOVACERAMIC (32.5 × 20 × 10 cm); APLANADO ≤ 1.5 cm POR CARA. LA FICHA TECNICA DEL FABRICANTE ACREDITA f'_an ≥ 0.50
10 LA LOCALIZACION DEL REMATE DEL ESTRIBO DE CUALQUIER ELEMENTO DEBERA ALTERNARSE DE UNO A OTRO LADO DEL MISMO
11 NO TOMAR MEDIDAS A ESCALA. LAS COTAS RIGEN AL DIBUJO. COTAS Y ARMADOS EN cm, TAMBIEN EL ACERO; NIVELES EN m
12 PROPUESTA DE ANTEPROYECTO PARA TRAMITE DE SEGURO. LIMITACIONES Y SUPUESTOS DECLARADOS EN LA MEMORIA DE CALCULO
13 EL ORIGINAL DE ESTE PLANO ES PROPIEDAD Y RESPONSABILIDAD EXCLUSIVA DEL CALCULISTA QUE FIRMA ESTA COPIA, CUALQUIER MODIFICACION DE SECCIONES, ARMADOS Y/O MODIFICACIONES ARQUITECTONICAS, DEBERAN SER PREVIAMENTE CONSULTADAS AL CALCULISTA, EL CUAL DARÁ SU APROBACIÓN O RECHAZO POR ESCRITO, DOCUMENTO QUE SE ANEXARA A ESTE PLANO, EN CASO DE NO SER ASÍ, EL CALCULISTA SE VERÁ LIBERADO DE TODA RESPONSABILIDAD INHERENTE A ESTE PROYECTO
14 EL CONSTRUCTOR DE LA OBRA, SERÁ EL RESPONSABLE DE LA CORRECTA INTERPRETACIÓN DEL PLANO, ASÍ COMO DE LA CALIDAD Y CARACTERÍSTICAS DE LOS MATERIALES EMPLEADOS, TANTO POR SU PERSONAL, COMO POR LOS SUBCONTRATISTAS Y DESTAJISTAS QUE INTERVENGAN EN LA EJECUCION DE LA OBRA
15 EL PROPIETARIO Y EL OCUPANTE DE LA CONSTRUCCIÓN, SERÁN LOS RESPONSABLES DEL USO DE LA MISMA, Y DE QUE LAS CARGAS VIVAS ESTIPULADAS EN LOS PLANOS NO SEAN EXCEDIDAS

CLAVE DE ELEMENTOS

- PANTALLA, ZAPATA Y DENTELLON DE CONCRETO
- BARDA DE NOVABLOCK MULTIPERFORADO 10
- CASTILLO Y DALA DE LA BARDA
- POR DEMOLER (BARDA CAIDA)

PROYECTO ESTRUCTURAL

M.I. FRANCISCO JAVIER CISNEROS RUIZ
CED. PROF. 15747504
MAESTRIA EN ESTRUCTURAS, UNAM

PROYECTO: MURO DE CONTENCION

PROPIETARIO

ESTADO: ANTEPROYECTO

UBICACION: COATEPEC, VER.

PLANO DE: CORTES Y DETALLES

FECHA: OCTUBRE 2026

ACOTACIONES: CENTIMETROS

ESCALA: INDICADA

CLAVE DE PLANO: E-3